

FLOW SHEET SCHISTE CALCINE – REV 1

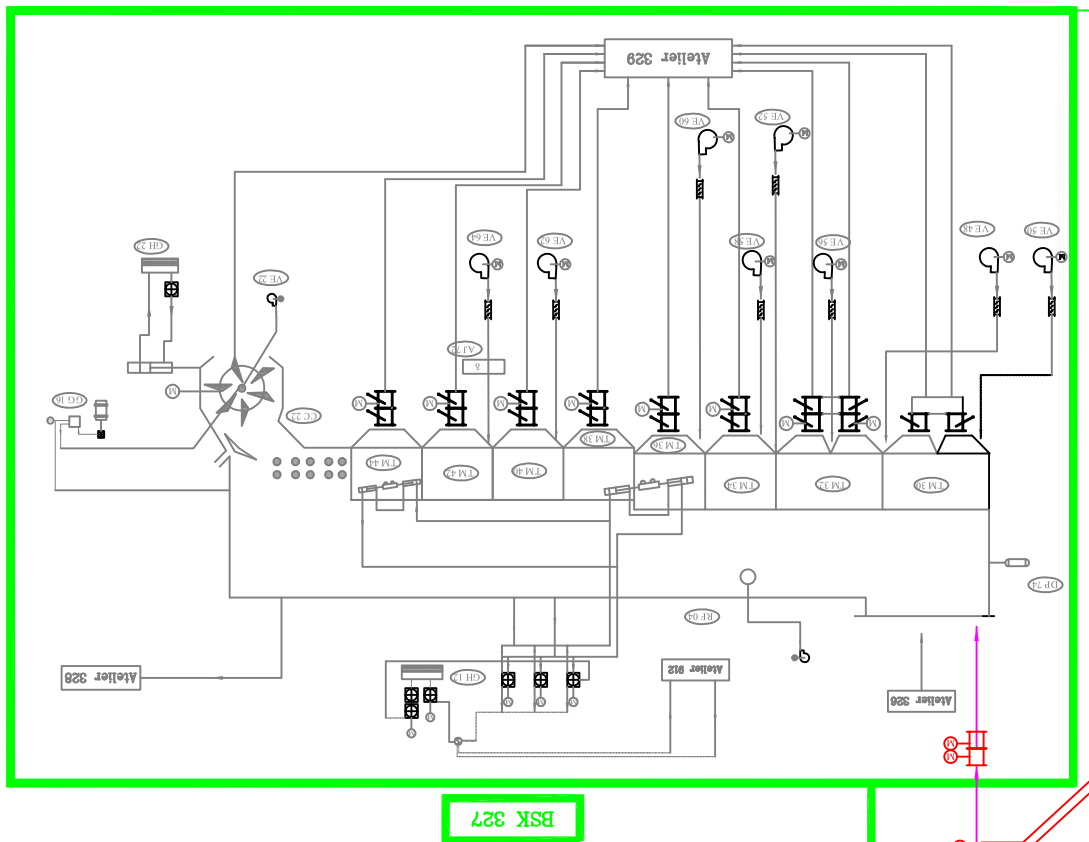

BSK 327

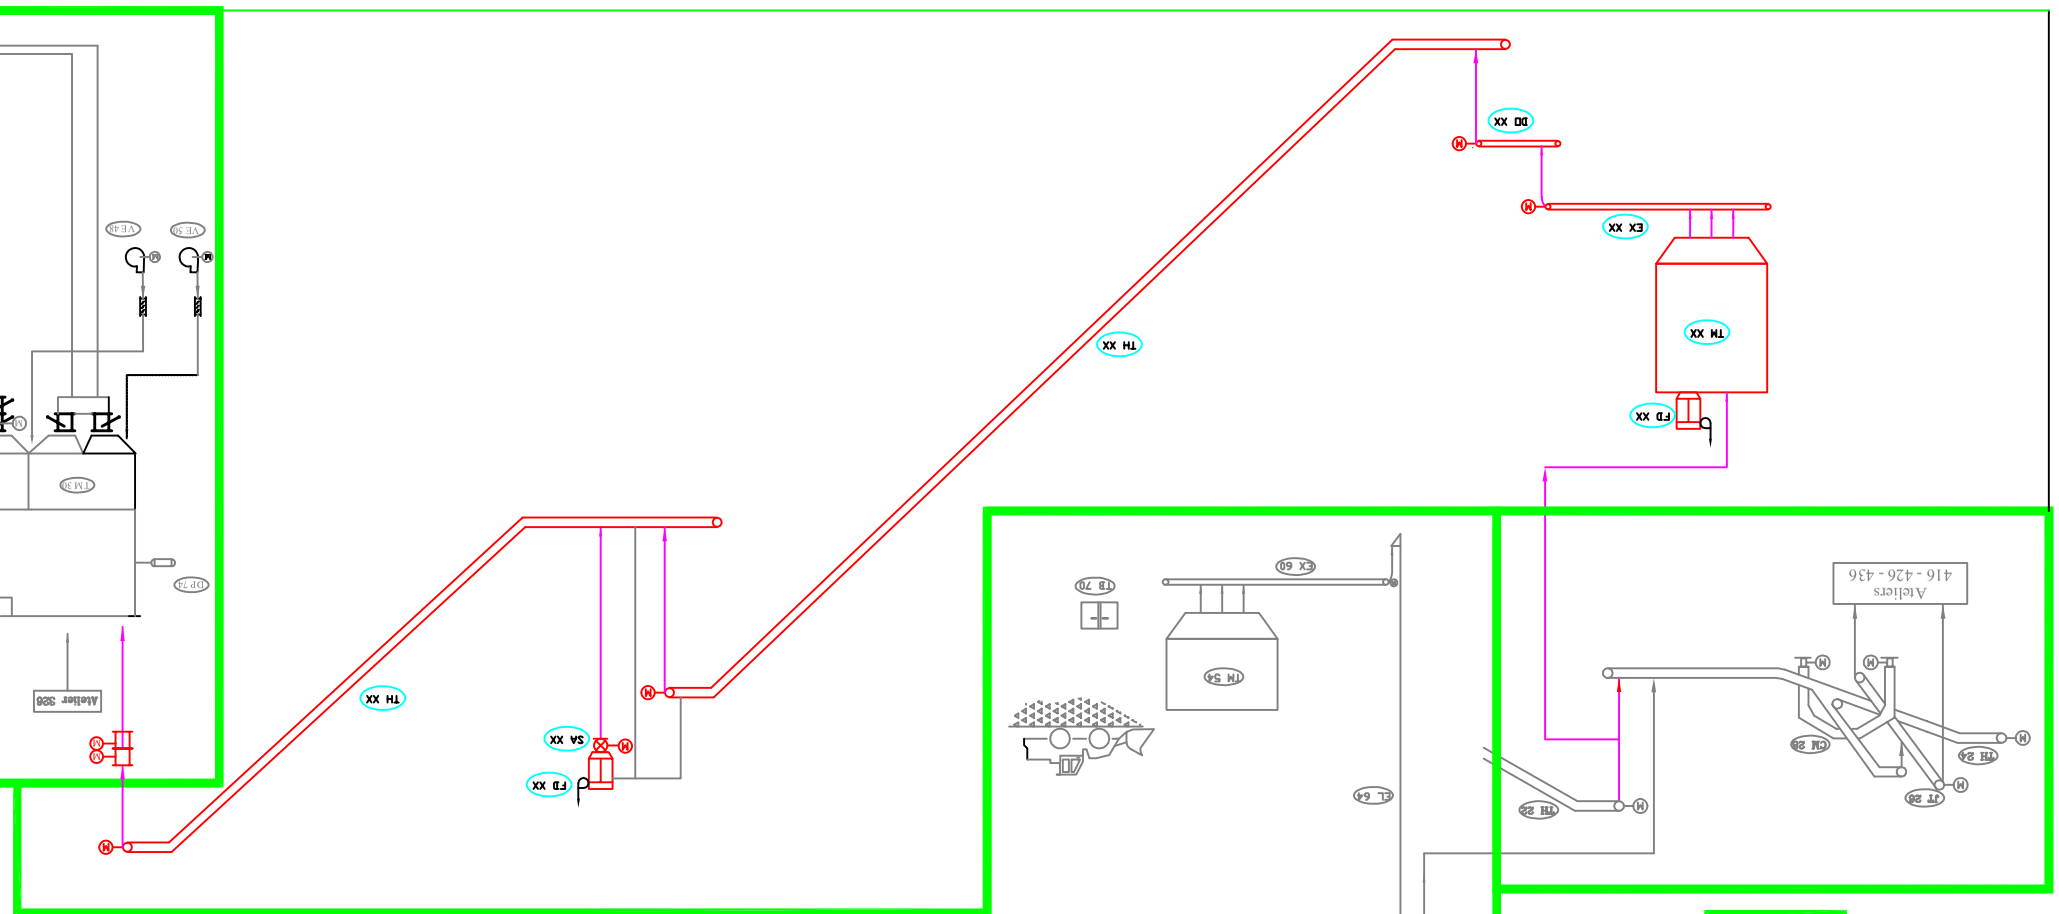

PROJET

BSK 402

BSK 115